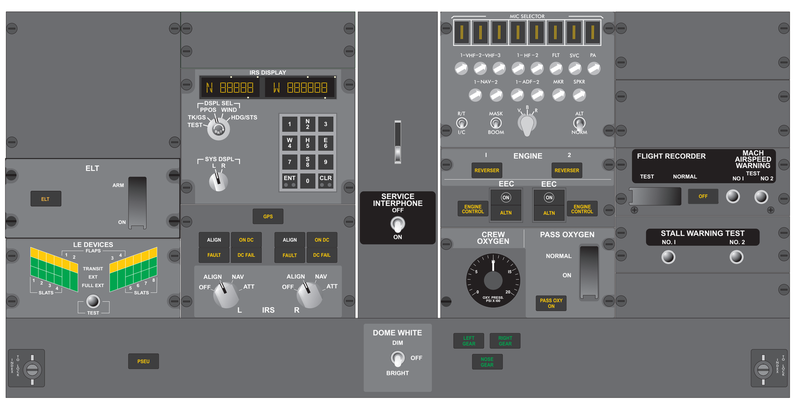

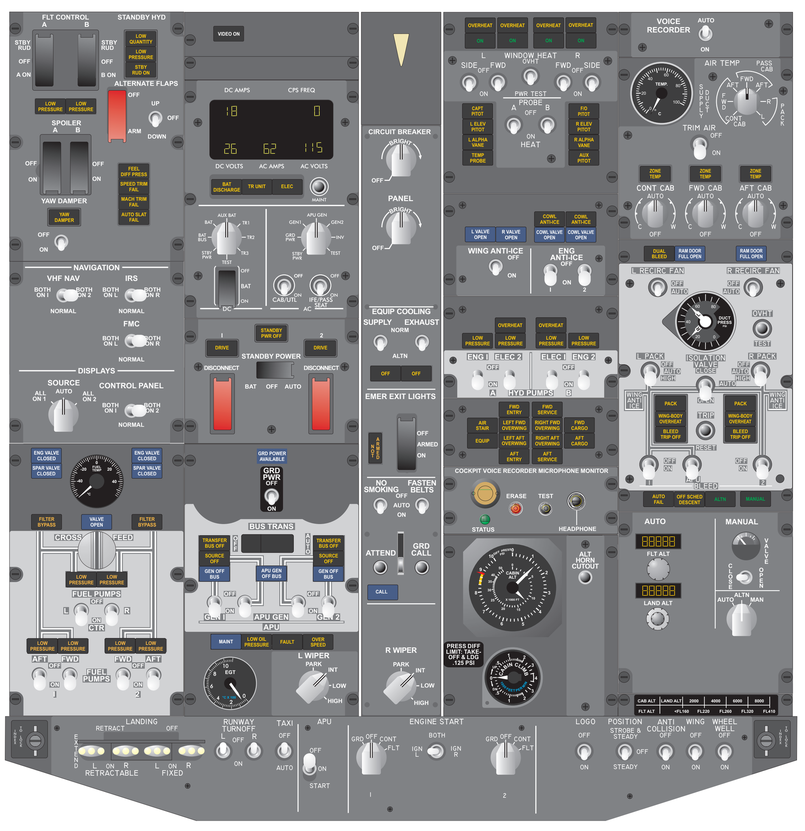

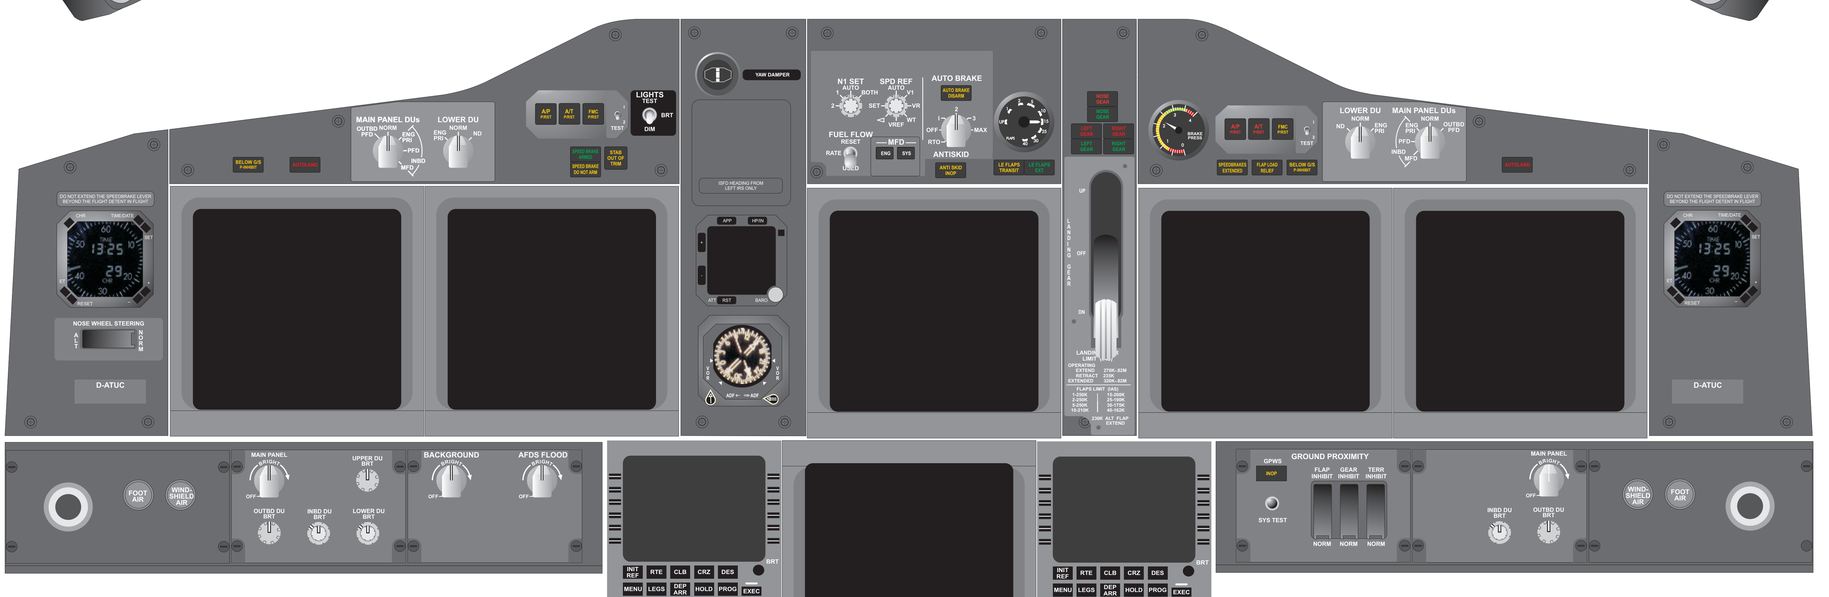

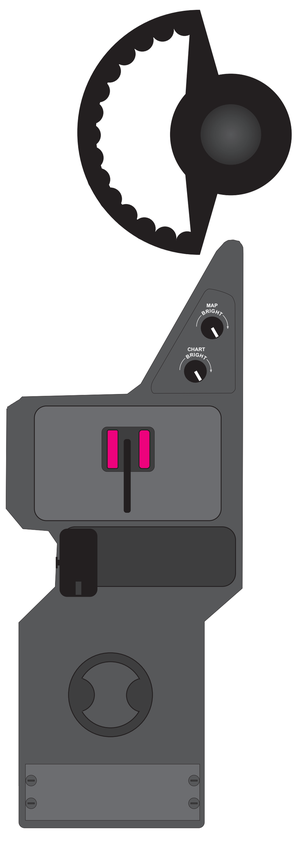

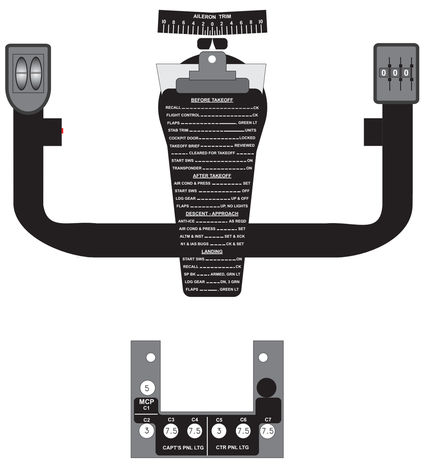

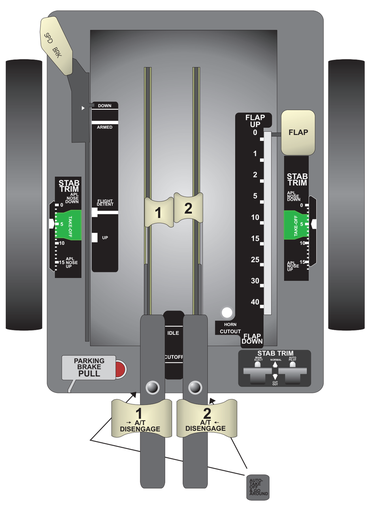

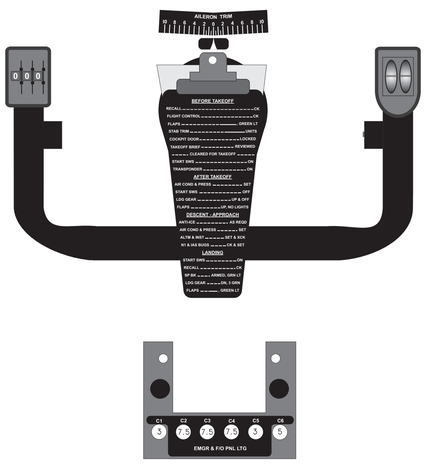

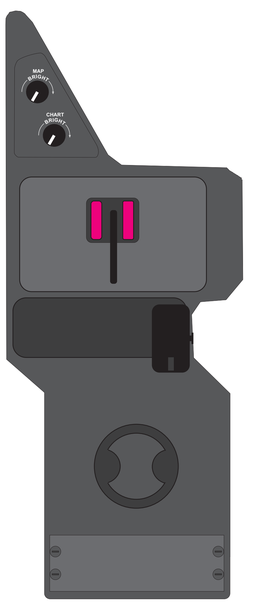

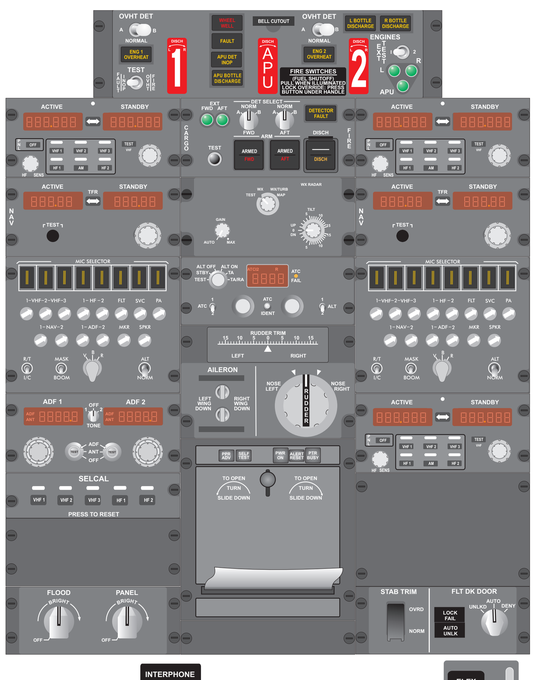

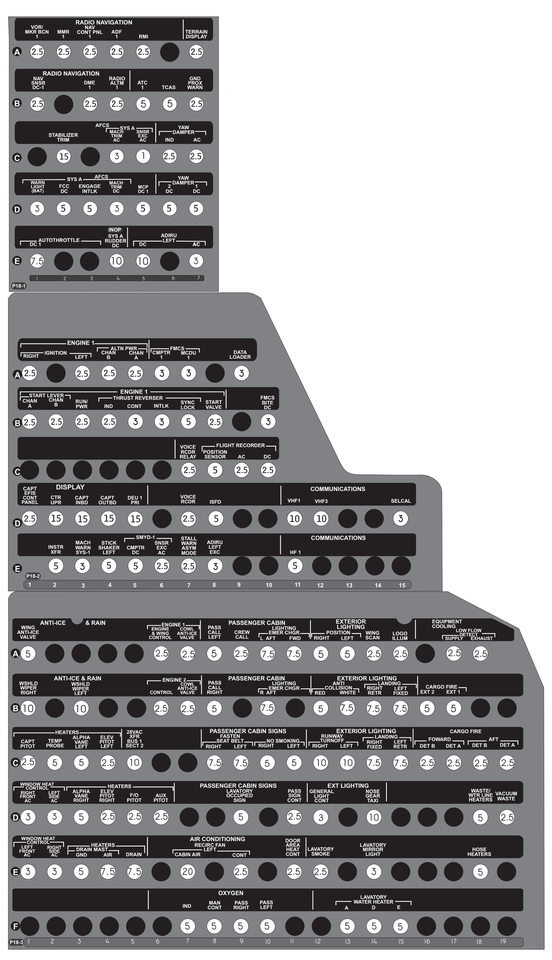

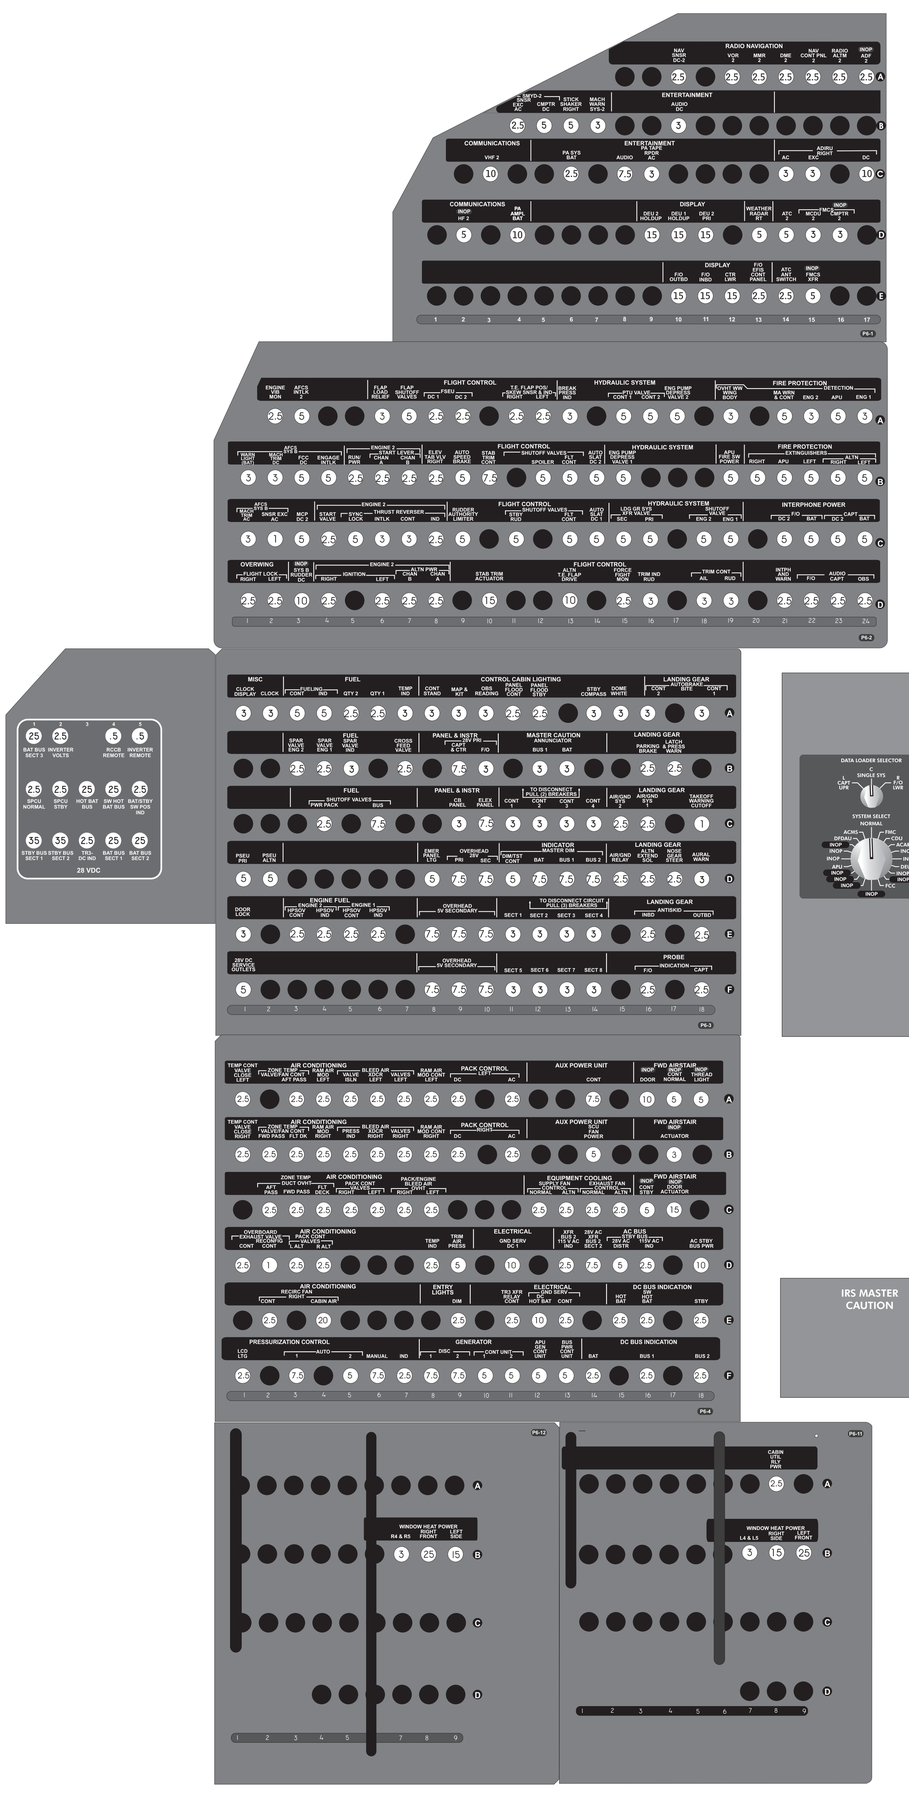

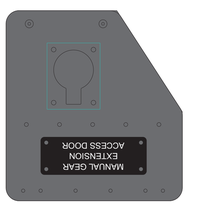
MANUAL SIDE
EXTENSION
ACCESS DOOR